




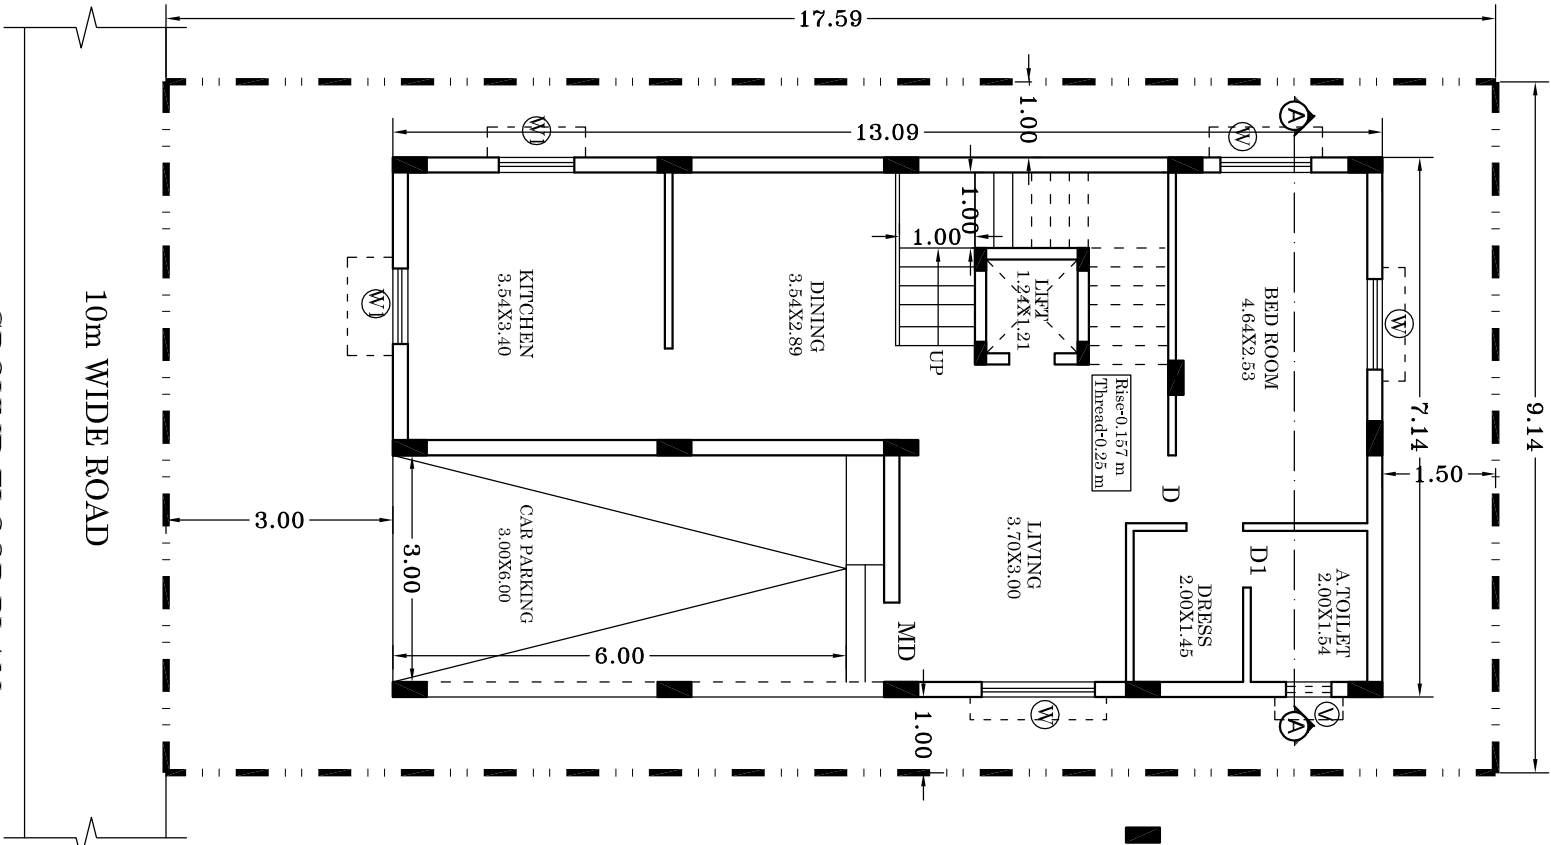


GROUND FLOOR PLAN

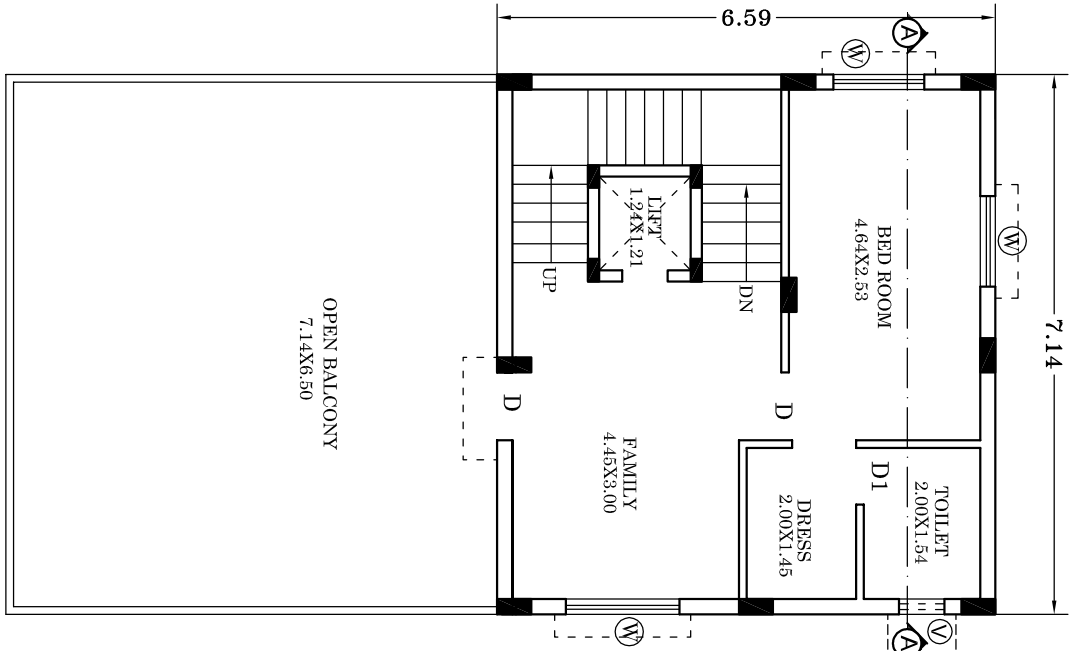


FIRST FLOOR PLAN

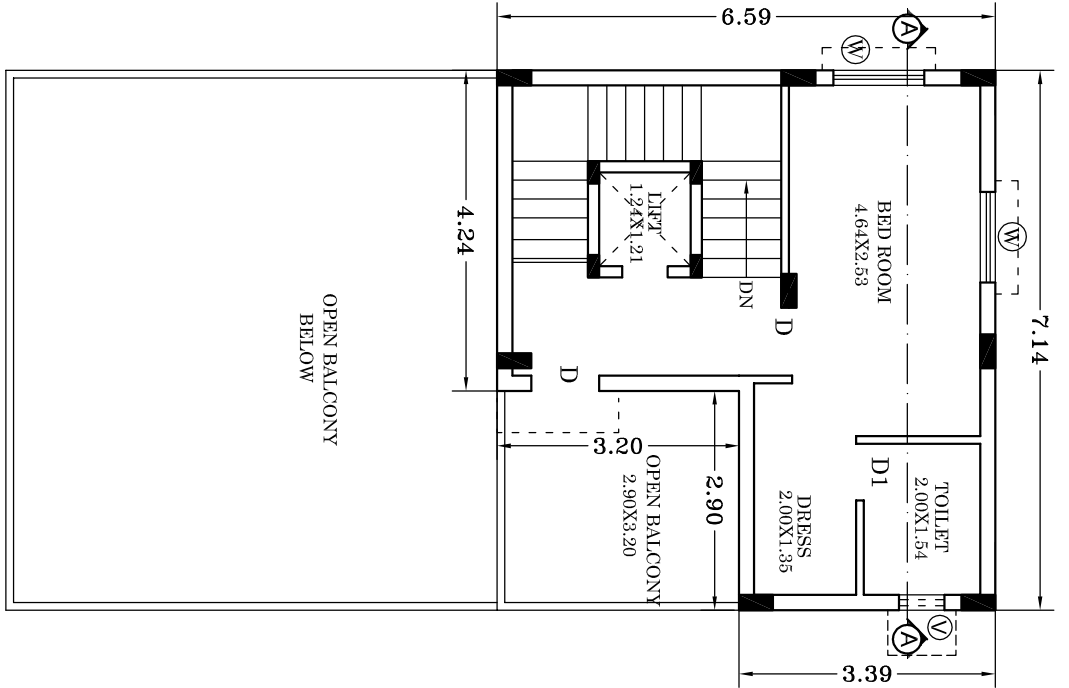


SECOND FLOOR PLAN

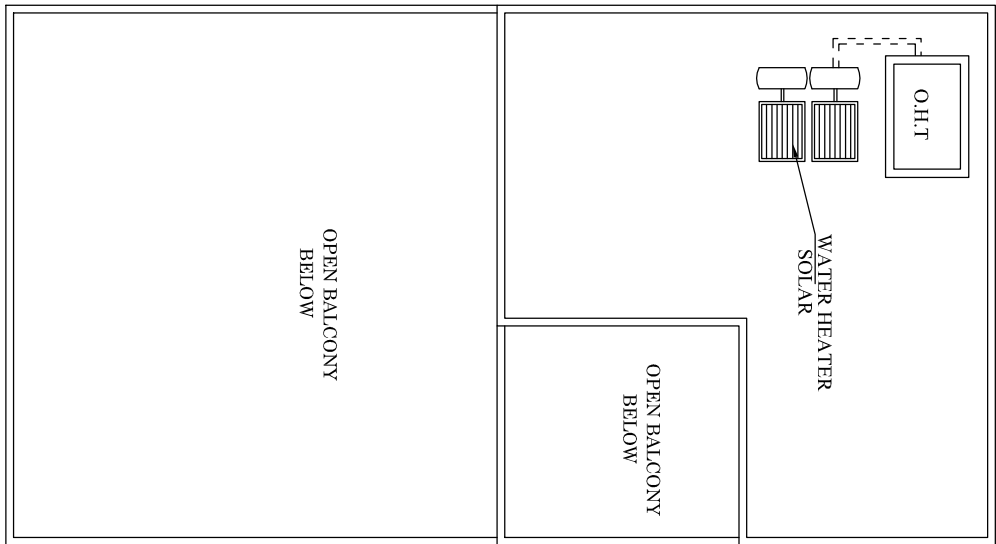


TERRACE FLOOR PLAN

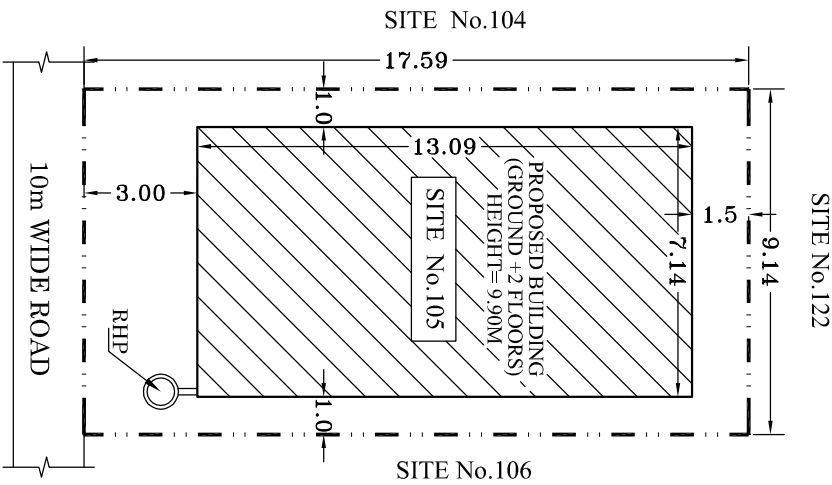

SITE PLAN SCALE 1:200

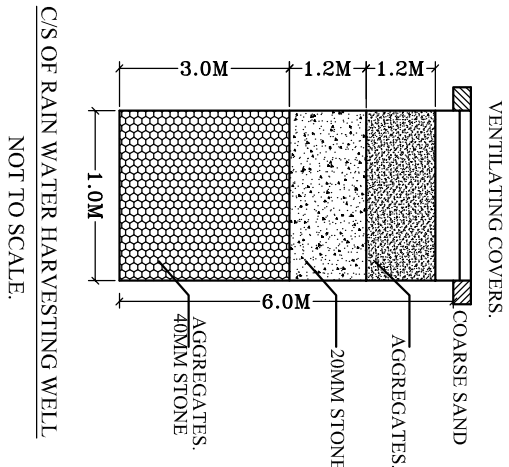

C/S OF RAIN WATER HARVESTING WELL
NOT TO SCALE.

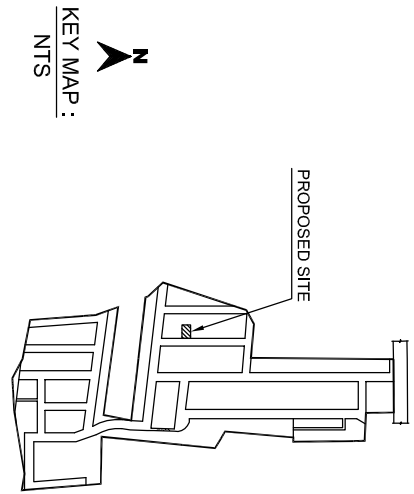

KEY MAP :
NTS



SCALE : 1:100

ALL DIMENSIONS ARE IN METERS		
SCHEDULE OF OPENINGS		
TYPE	DESCRIPTION	SIZE
MD	MAIN DOOR	1.05 X 2.10
D	DOOR	0.90 X 2.10
D1	DOOR	0.75 X 2.10
PD	PULL DOOR	0.90 X 2.10
W1	WINDOW	1.20 X 1.20
W2	WINDOW	1.00 X 1.20
V	VENTILATOR	0.60 X 0.60

AREA STATEMENT
SITE AREA : 160.77 Sq.m

BUILT UP AREA STATEMENT (IN Sq.m)				
SL. NO.	FLOOR	GROSS BUILT UP AREA	DEDUCTIONS	NET F.A.R AREA
		1	2	3
			PARKING	BALCONY
1	Ground	93.46	18.00	18.00
2	First	47.05		0.00
3	Second	37.77		0.00
4	Terrace	0.00		0.00
Grand Total		178.28		18.00
GROSS BUILT UP AREA				
NET F.A.R AREA				
GROUND COVERAGE AREA				

SANCTIONING AUTHORITY

Mrs. AMULYA S.N

ENGINEER'S SIGNATURE

BASAYYA S.K

BCC/BL/3.6/S-1415/2014-15

BHC triangle

4-56, 3rd Floor, Kengeri Main Road, Bengaluru, 560019
E-mail: bhctriangle@gmail.com

PROJECT NAME

PROPOSED RESIDENTIAL BUILDING PLAN IN
SITE No. 105, KHATA No. 846/105 (15020030220200893)
IN SY No. 103/14, 103/1 & OTHERS OF B.M.KAVAI VILLAGE
& Sy.No. 15/2 & OTHERS OF RACHANAMADU VILLAGE
KENGERI HOBLI, BENGALURU SOUTH TALUK,
BENGALURU DISTRICT.